



REV	DESCRIPTION	DATE	BY
P1	Making sketch for the prototype build plan	2026-10-03	AC

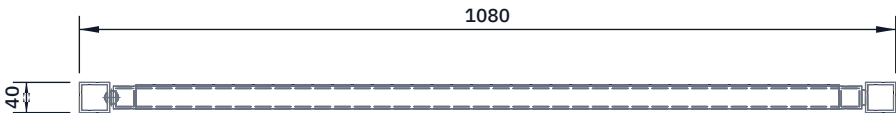

TOP VIEW
Scale 1:10; looking down (along -Z)

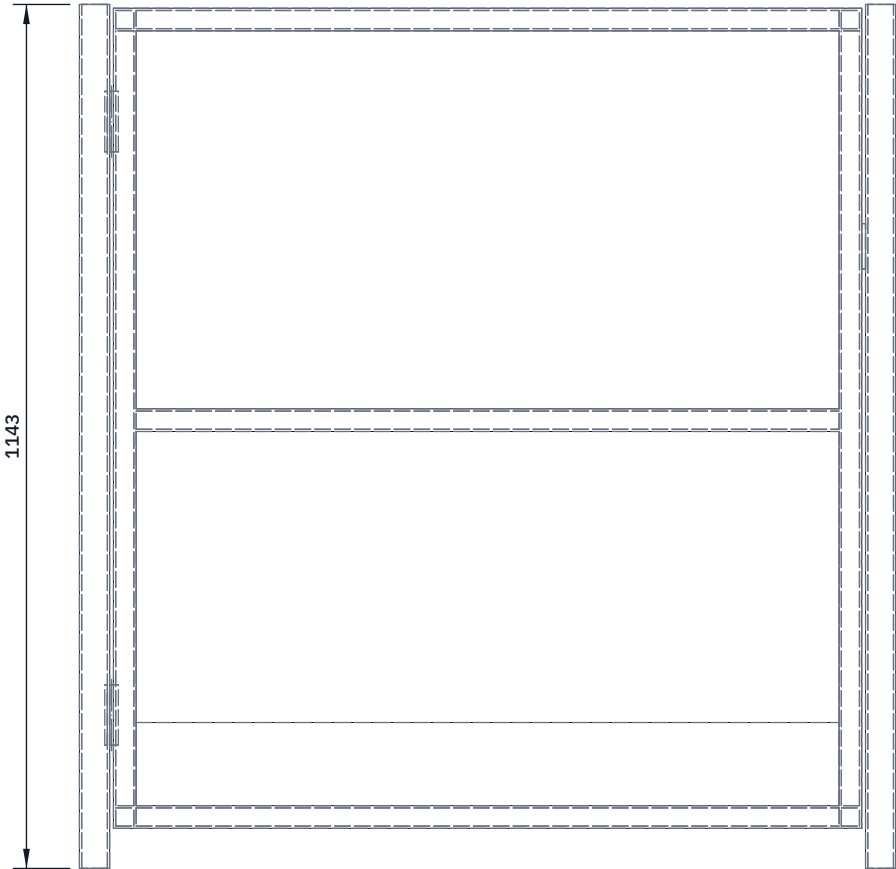

FRONT VIEW
Scale 1:10; looking at the front (along +Y)



RIGHT VIEW
Scale 1:10; looking at the right side (along -X)



WHERE IT GOES
This part in colour, its neighbours in grey

HOW TO MAKE IT AND HOW IT FITS

- Posts: SHS 40 x 40 x 3, 1,143 mm, one bolted to the inside of each truss end vertical with three M12 bolts.
- Gate leaf (drawn): 30 x 30 x 3 frame 1,070 x 1,075 mm, knee rail at 550 mm above the floor, 2 mm toe plate 150 mm tall, 5 mm clear of each post and 10 mm above the floor.
- Hinges: two self-closing spring hinges on the side A post; the gate opens inward onto the deck only, never out over the drop.
- Latch: gravity latch on the side B post at 750 mm above the floor.
- Inner end rail: same posts with a fixed top rail, knee rail and toe plate, all welded, bolted to the inner end verticals.
- Check: gate closes and latches by itself from 90 degrees open.

KILNDECK			github.com/BoujeeEnjinia1701/kilndeck		
KilnDeck outer end gate and inner end rail: making sketch					
DRAWING NO. KND-DWG-106			REV P1	SHEET 1 of 1	SIZE ANSI B
SCALE 1:10	UNITS mm	PROJECTION 	DATE 2026-10-03		DRAWN Amish Chadha
MATERIAL / NOTES SHS 40 x 40 x 3 and 30 x 30 x 3 mm; 2 mm sheet; spring hinges; S275					
Licensed CERN-OHL-S-2.0 · Design Molecule Lab · designmolecule.com			Generated from cad/src; do not edit by hand		