BUILD PLAN SKETCH, PLAN NOT YET BUILT KilnDeck · github.com/BoujeeEnjinia1701/kilndeck

REV	DESCRIPTION	DATE	BY
P1	Making sketch for the prototype build plan	2026-10-03	AC

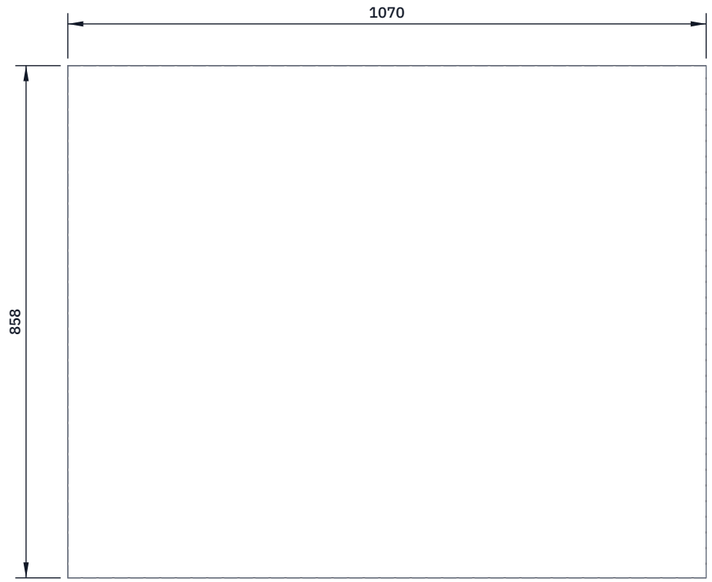

TOP VIEW

Scale 1:10; looking down (along -Z)

FRONT VIEW

Scale 1:10; looking at the front (along +Y)

RIGHT VIEW

Scale 1:10; looking at the right side (along -X)

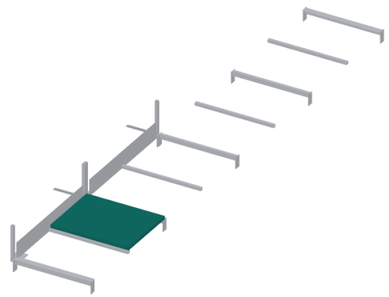

WHERE IT GOES

This part in colour, its neighbours in grey

HOW TO MAKE IT AND HOW IT FITS

Make eight, 1,070 mm across the deck by about 858 mm (end panels 818 mm). Panel 1 at the gate end has a 86 x 46 mm notch for the hand wheel chain case.

Frame: 40 x 40 x 4 angle welded into a rectangle, legs inward.

Underside: 1 mm aluminium sheet riveted under the frame, bright side down, to reflect heat from the crust. Do not paint it.

Board: 37 mm calcium silicate cut to fit inside the frame, dry.

Top: 2 mm steel sheet stitch welded to the frame, light grey anti-slip coating. Drill two 10 mm drain holes at the low corner.

Fit: rests on two bearers, 2 mm gap to the next panel and 5 mm to the toe boards; two M8 bolts each end into the bearers.

Check: about 30 kg; flat within 3 mm; no gap in the board.

KILNDECK github.com/BoujeeEnjinia1701/kilndeck

KilnDeck insulated floor panel (make 8): making sketch

DRAWING NO.	REV	SHEET	SIZE
KND-DWG-105	P1	1 of 1	ANSI B

SCALE	UNITS	PROJECTION	DATE	DRAWN
1:10	mm		2026-10-03	Amish Chadha

MATERIAL / NOTES

40 x 40 x 4 angle; 2 mm steel sheet; 37 mm calcium silicate board; 1 mm aluminium

Licensed CERN-OHL-S-2.0 · Design Molecule Lab · designmolecule.com

Generated from cad/src; do not edit by hand