
CONCEPT, NOT FOR FABRICATION


KilnDeck · github.com/BoujeeEnjinia1701/kilndeck

REV	DESCRIPTION	DATE	BY
P1	Concept sheet from the constructable TRL 3 model	2026-10-03	AC

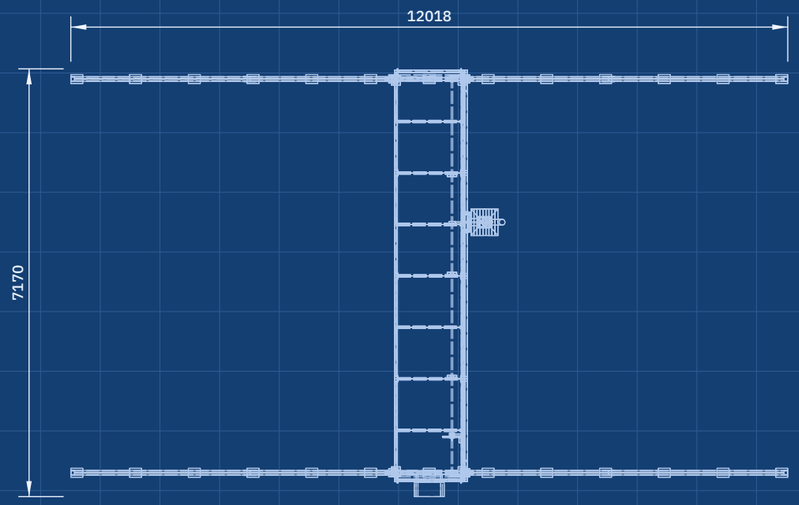


TOP VIEW

Scale 1:100; looking down (along -Z)

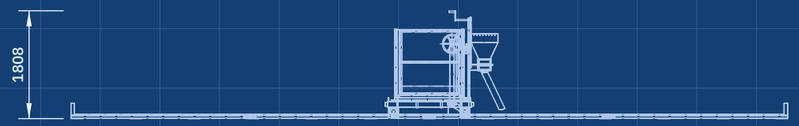


FRONT VIEW

Scale 1:100; looking at the front (along +Y)

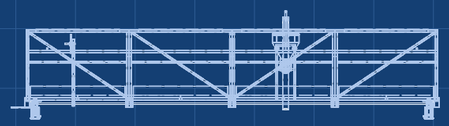

RIGHT VIEW

Scale 1:100; looking at the right side (along -X)

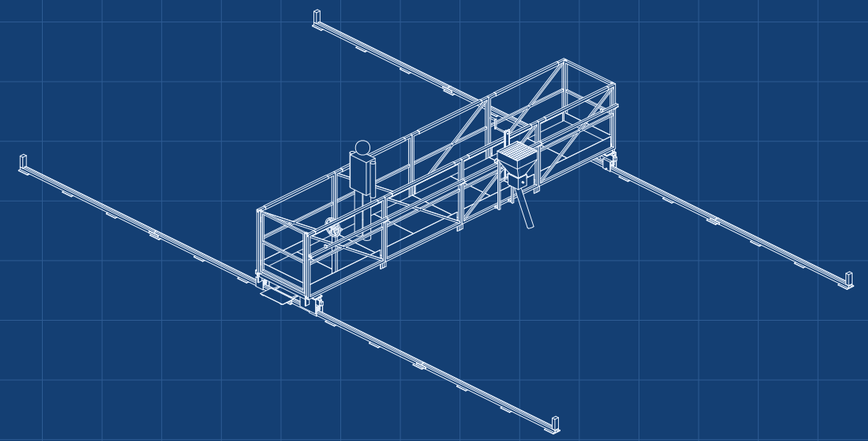

ISOMETRIC VIEW

Not to scale; figure is a 1.75 m person on the deck; seen from the front right and above, about 30 deg elevation

KEY FIGURES

- Deck spans 6.6 m between wall-top tracks
- Floor 393 mm above the wall top; 1.1 m guardrails
- Deck about 810 kg; no piece over 40 kg
- Rated load 250 kg; hand wheel force about 65 N
- Hopper 52 L, about 42 kg of coal
- Rotor about 0.49 kg of coal per pocket (est.)
- Insulated floor: steel, 37 mm board, aluminium
- Manual only: no motor, no power on the kiln

KILNDECK

github.com/BoujeeEnjinia1701/kilndeck

Rolling fuel-feeding deck for brick kilns, concept

DRAWING NO.	REV	SHEET	SIZE
KND-DWG-010	P1	1 of 1	ANSI B

SCALE	UNITS	PROJECTION	DATE	DRAWN
1:100	mm		2026-10-03	Amish Chadha

MATERIAL / NOTES

Concept sheet from the D3 model (kit 1.9)

Licensed CERN-OHL-S-2.0 · Design Molecule Lab · designmolecule.com

Generated from cad/src; do not edit by hand