BUILD PLAN SKETCH, PLAN NOT YET BUILT

KilnDeck · github.com/BoujeeEnjinia1701/kilndeck

REV	DESCRIPTION	DATE	BY
P1	Making sketch for the prototype build plan	2026-10-03	AC

TOP VIEW

Scale 1:10; looking down (along -Z)

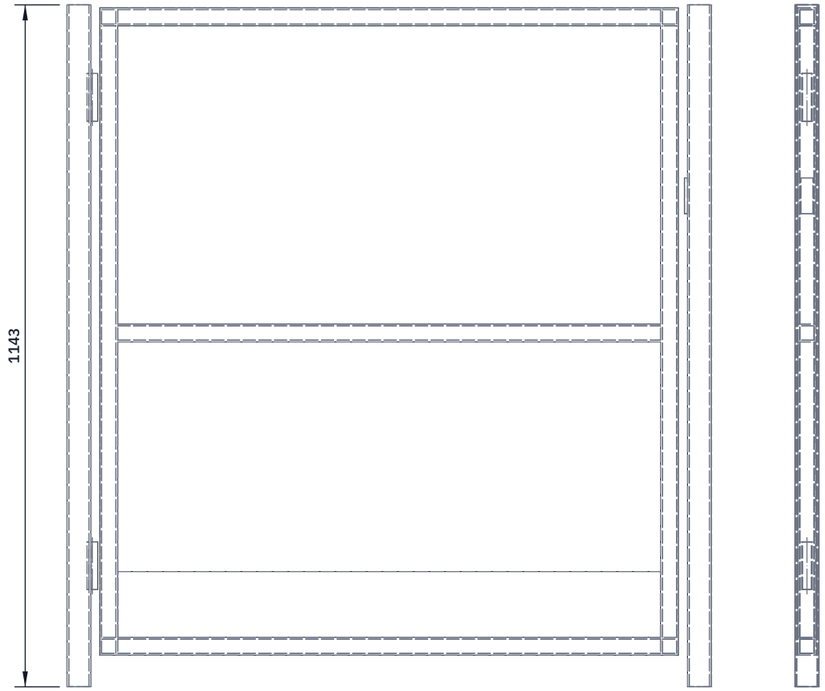

FRONT VIEW

Scale 1:10; looking at the front (along +Y)

RIGHT VIEW

Scale 1:10; looking at the right side (along -X)

WHERE IT GOES

This part in colour, its neighbours in grey

HOW TO MAKE IT AND HOW IT FITS

Posts: SHS 40 x 40 x 3, 1,143 mm, one bolted to the inside of each truss end vertical with three M12 bolts.

Gate leaf (drawn): 30 x 30 x 3 frame 1,070 x 1,075 mm, knee rail at 550 mm above the floor, 2 mm toe plate 150 mm tall, 5 mm clear of each post and 10 mm above the floor.

Hinges: two self-closing spring hinges on the side A post; the gate opens inward onto the deck only, never out over the drop.

Latch: gravity latch on the side B post at 750 mm above the floor.

Inner end rail: same posts with a fixed top rail, knee rail and toe plate, all welded, bolted to the inner end verticals.

Check: gate closes and latches by itself from 90 degrees open.

KILNDECK

github.com/BoujeeEnjinia1701/kilndeck

KilnDeck outer end gate and inner end rail: making sketch

DRAWING NO.	REV	SHEET	SIZE
KND-DWG-106	P1	1 of 1	ANSI B

SCALE	UNITS	PROJECTION	DATE	DRAWN
1:10	mm		2026-10-03	Amish Chadha

MATERIAL / NOTES

SHS 40 x 40 x 3 and 30 x 30 x 3 mm; 2 mm sheet; spring hinges; S275

Licensed CERN-OHL-S-2.0 · Design Molecule Lab · designmolecule.com

Generated from cad/src; do not edit by hand